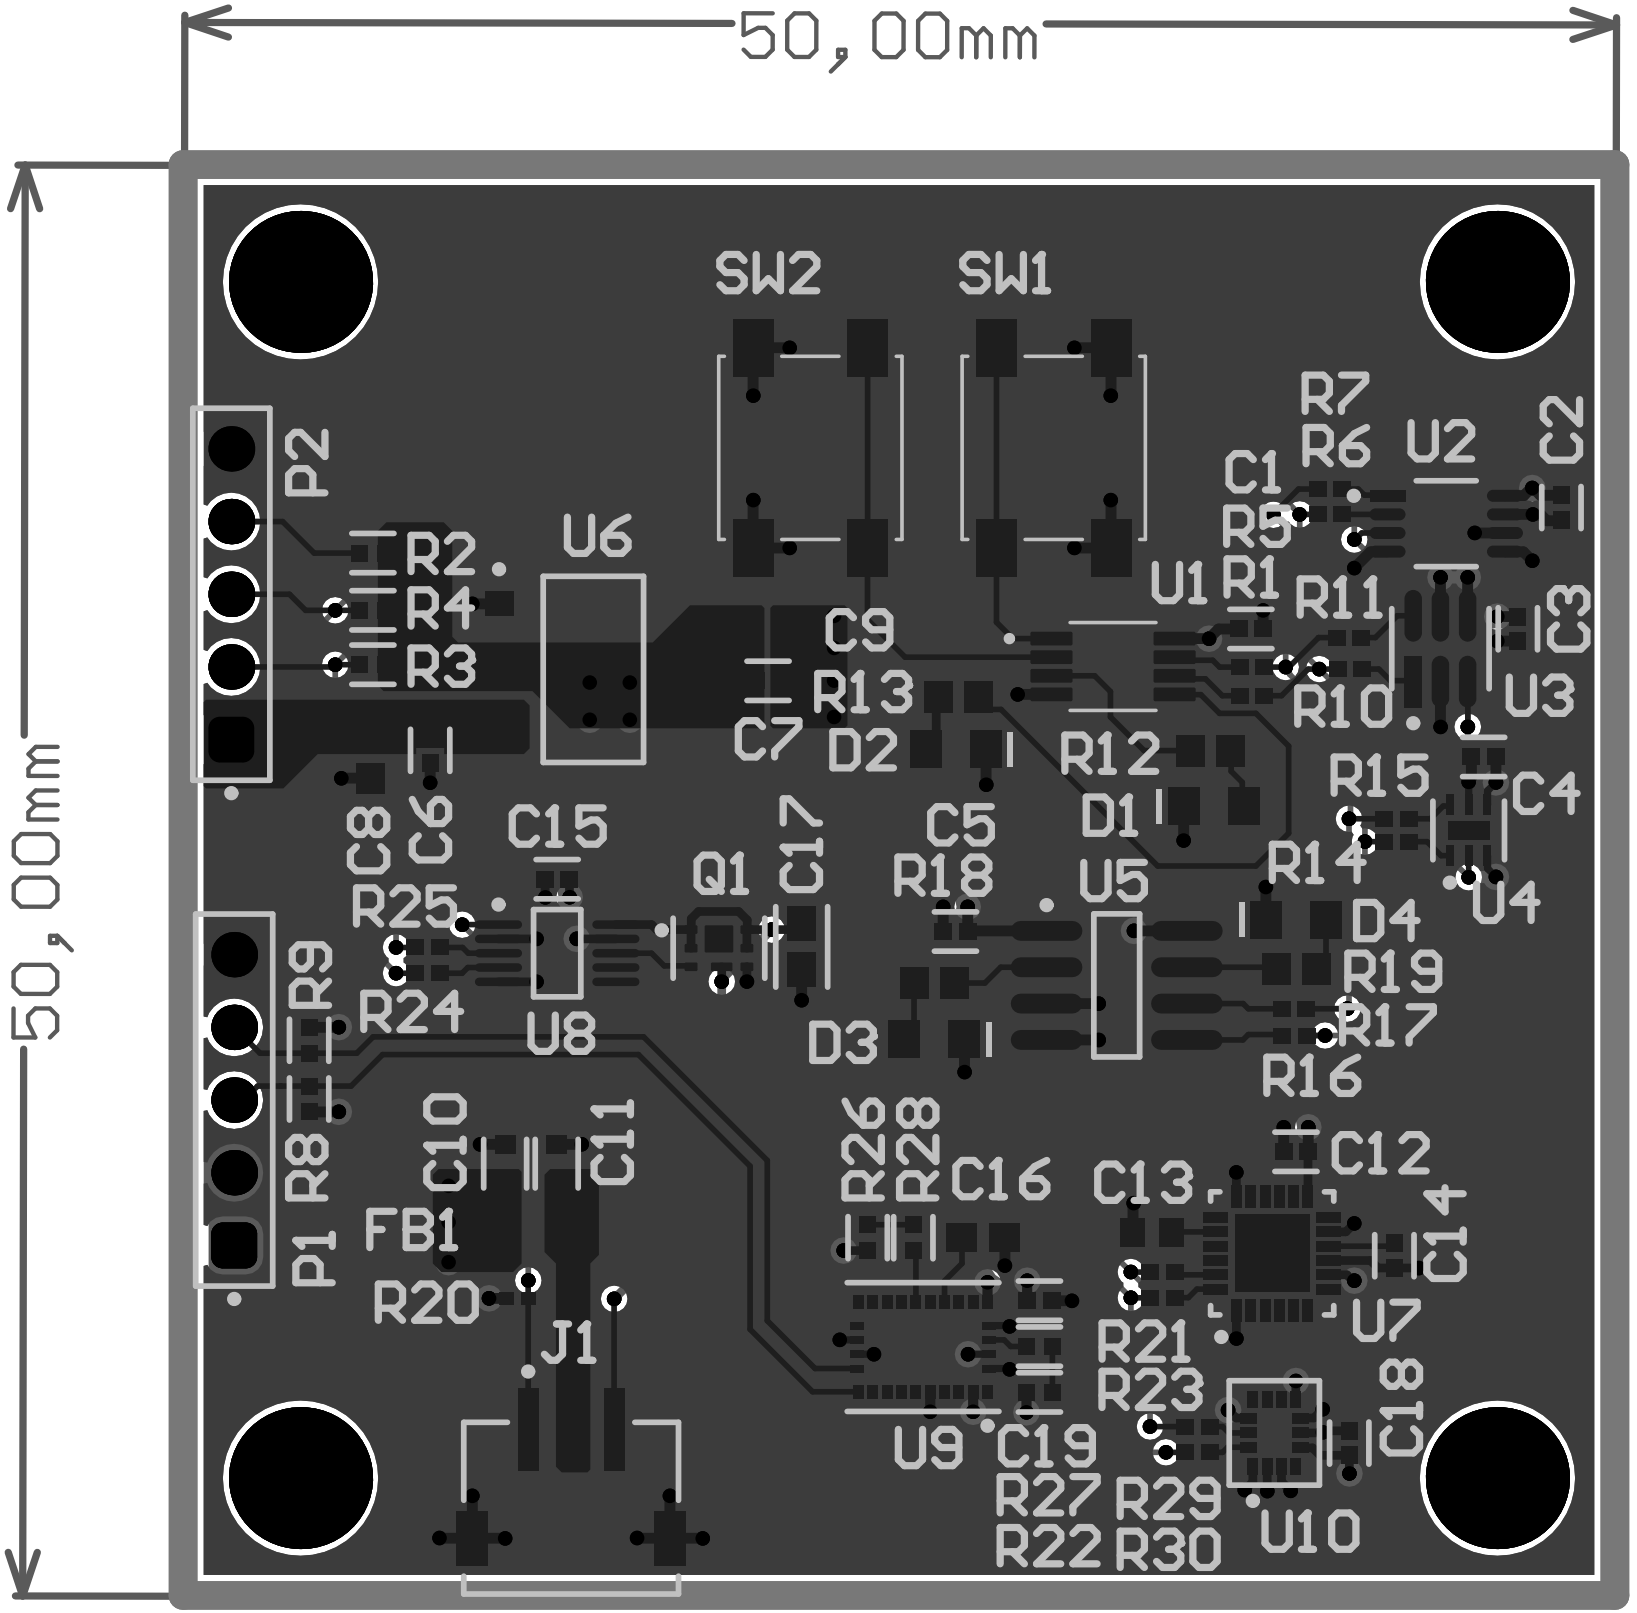

50,00mm
50,00mm
SW2
SW1
P2
U6
R2
R4
R3
C9
R13
C7
D2
U1
R7
R6
U2
C2
C1
R5
R1
R11
C3
U3
R10
R12
D1
R15
C4
U4
R14
D4
R19
R17
R16
C5
R18
U5
C15
Q1
C17
C8
C6
R25
R24
U8
R9
D3
P1
R8
C10
C11
FB1
R20
J1
R26
R28
C16
C13
C12
C14
U7
R21
R23
U9
C19
C18
R27
R29
R22
R30
U10